
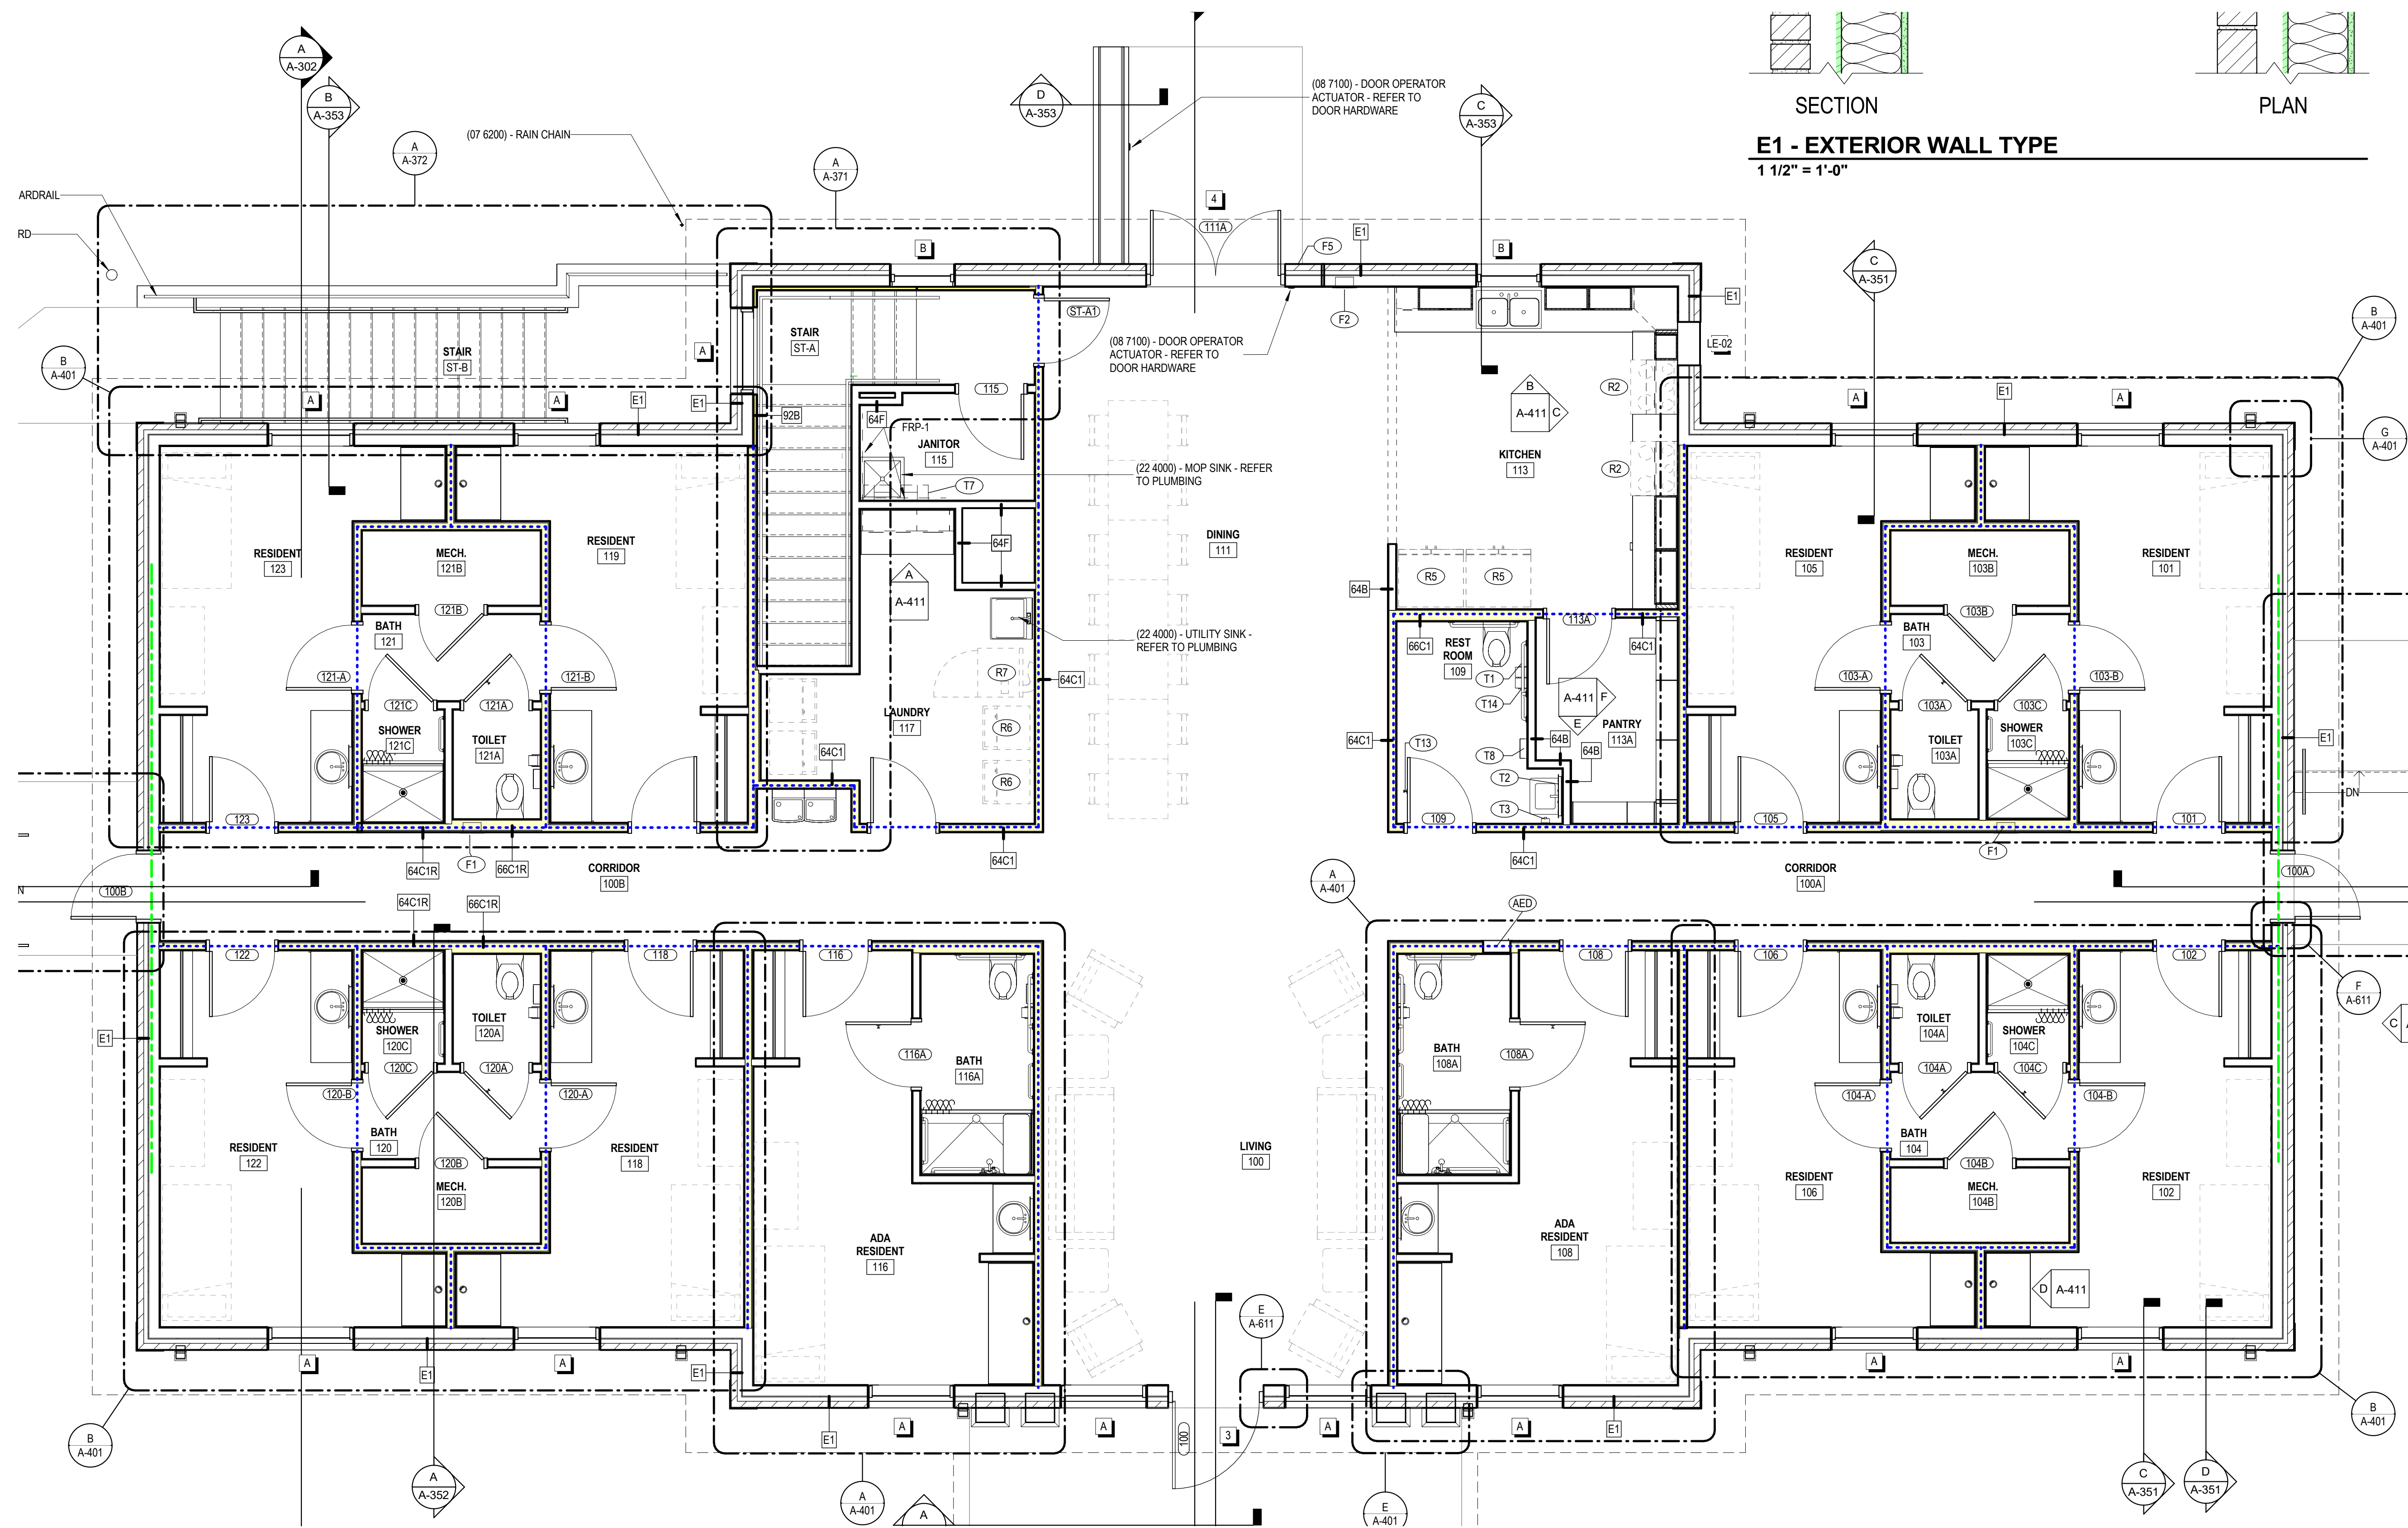


SECTION

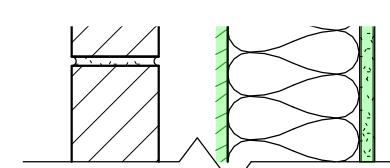

PLAN

E1 - EXTERIOR WALL TYPE
1 1/2" = 1'-0"