


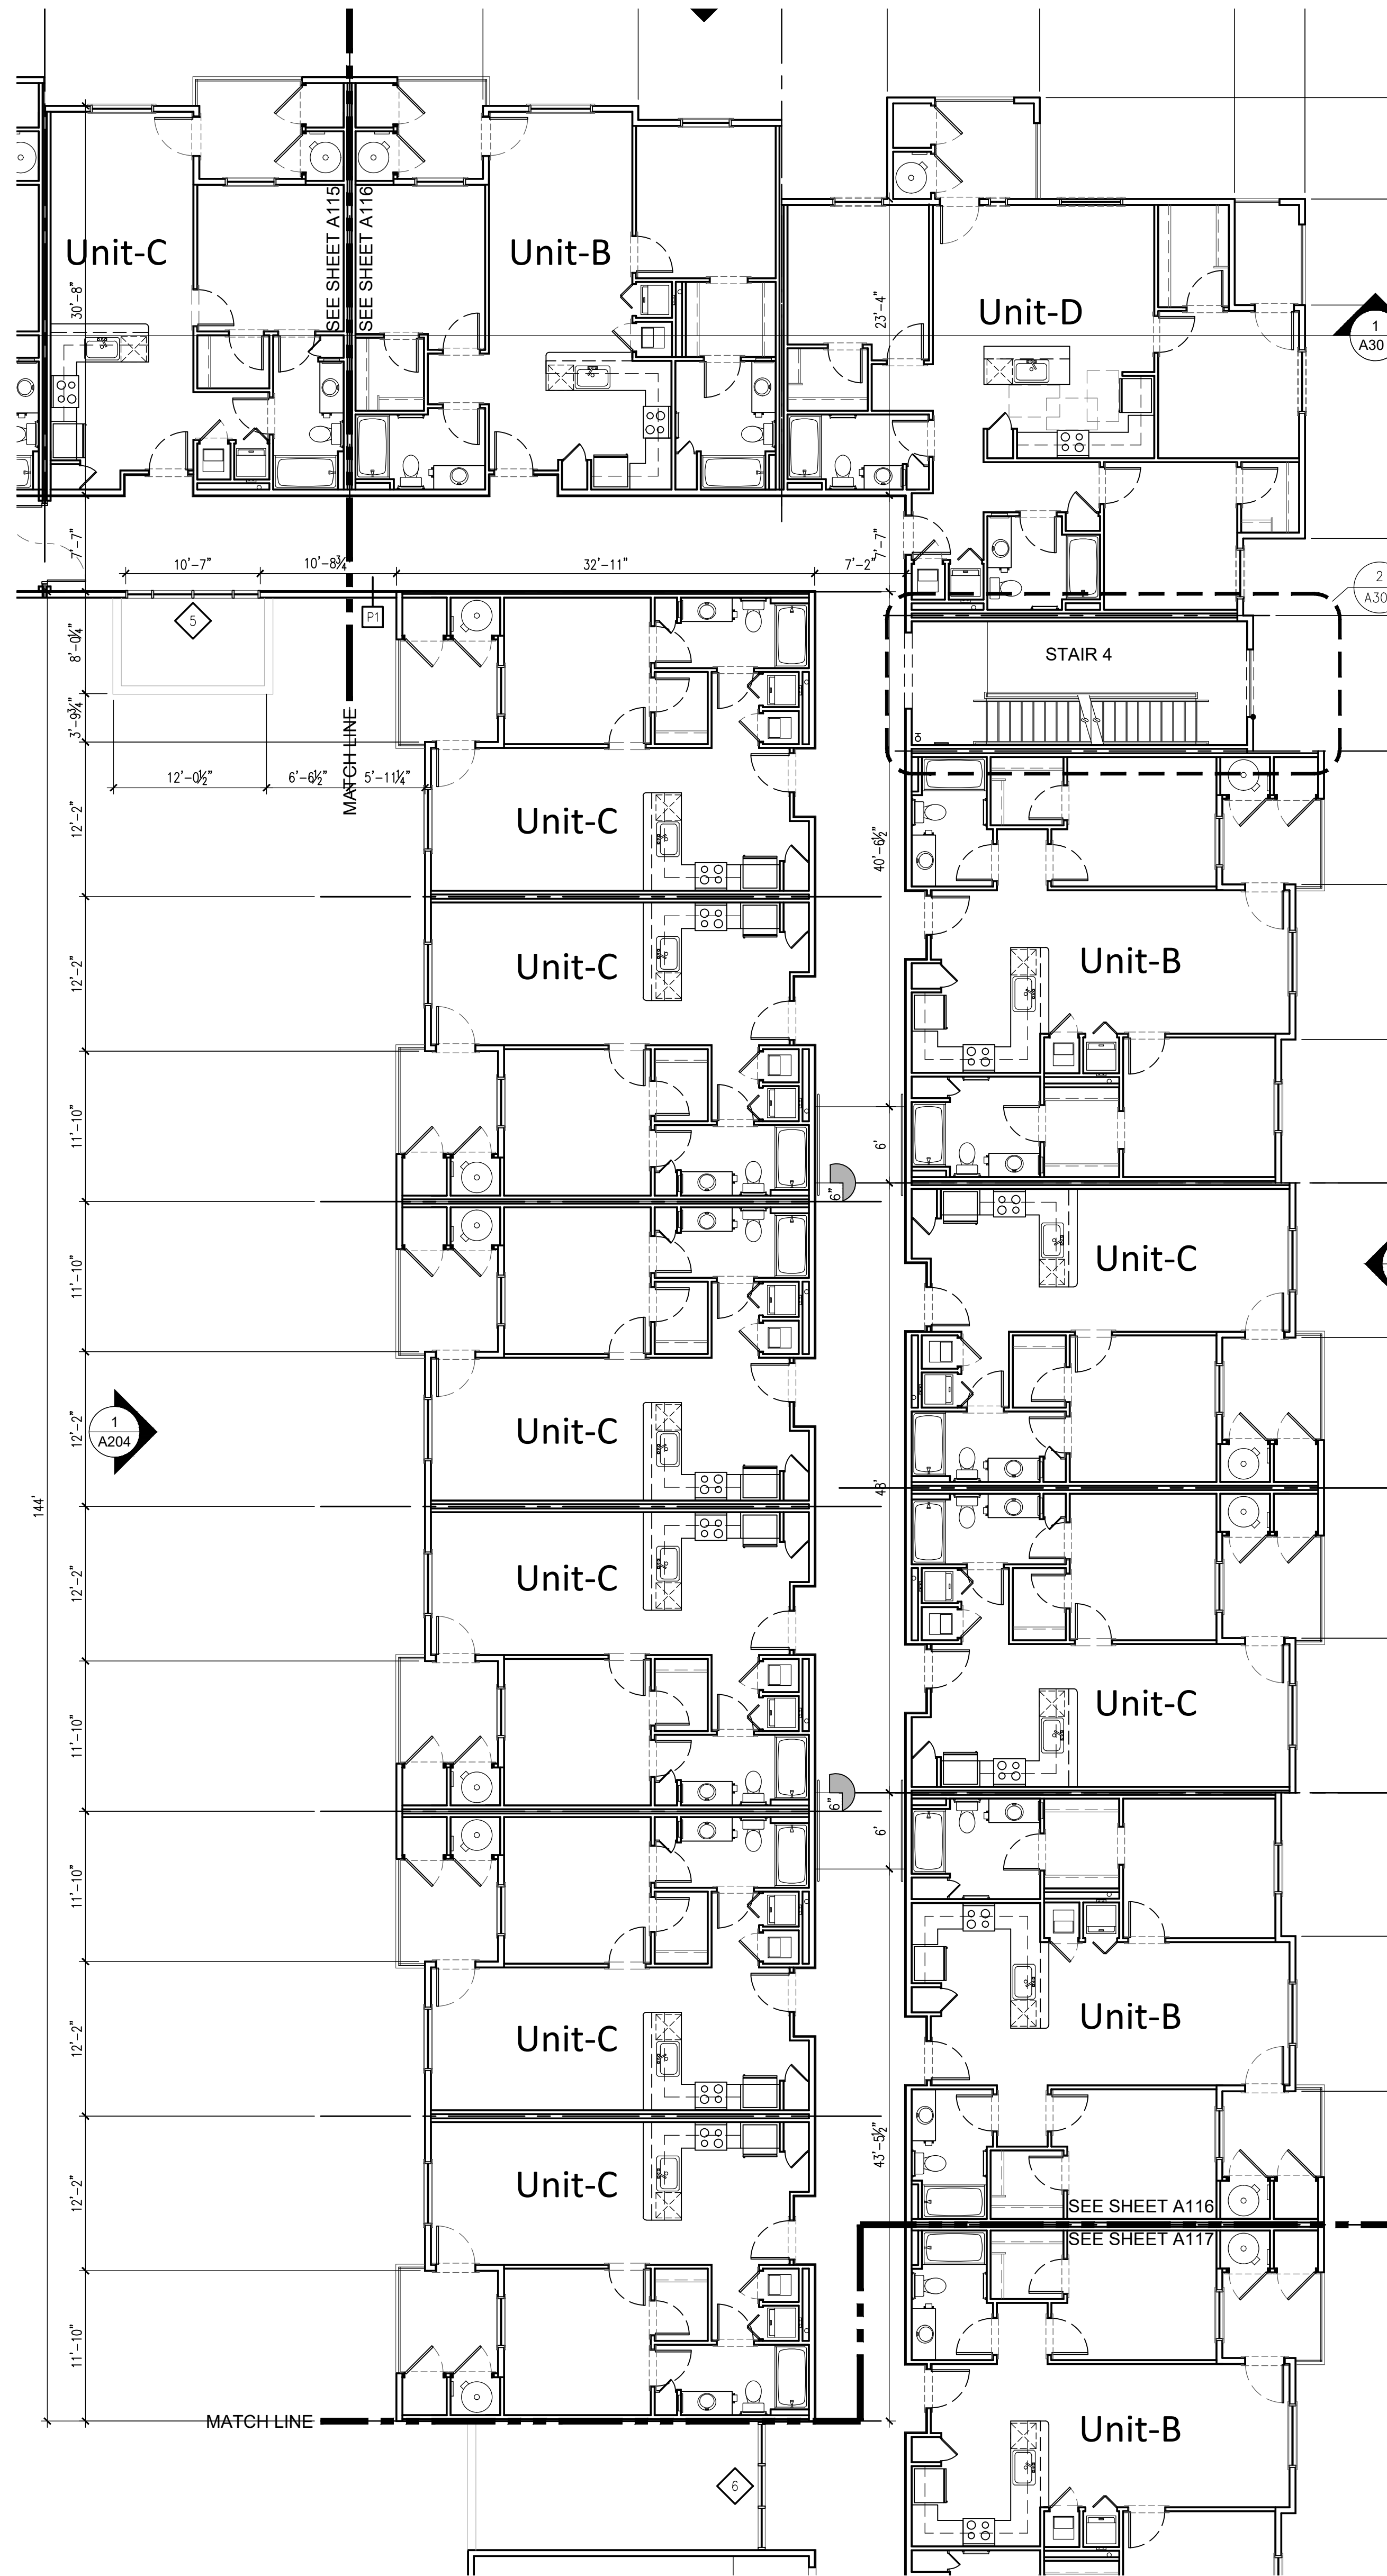

1 PARTIAL 2ND & 3RD FLOOR PLANS
SCALE: 1/8" = 1'-0"